PARSONS dar MBL MODERN BUILDING LEADERS (MBL) Co. LLC شركة قادة البناء الحديث المحدودة

Work Inspection Request

Request Ref.:	L01-MBLC-CON-ARC-WIR-010493	**Revision:**	R01	**Submission Date:**	09/03/24
Project:	L01-01	**Inspection Date:**	10/03/24	**Time:**	11:00
Client:	CPPA	**Project/Zone No:**	L01/17		
PMCM/Engineer:	Saudi Arabian Parsons Ltd	**Contractor:**	MBL		

Discipline:

☐ Survey ☐ Civil ☒ Architectural ☐ Structural ☐ Landscape
☐ Electrical ☐ Low current ☐ Mechanical ☐ HSE ☐ Testing/Commissioning
☐ Facade ☐ Others (.....) Sub- discipline (Steel Structure)

Work Details:

Description:
INSPECTION FOR (CEILING SUSPENTION SYSTEM) IN FIRST FLOOR ZONE 17- CORRIDOR 5: (FF-Z2-73)

Approved Method Statement:	L01-MBLC-CON-ARC-MES-006192-R00	**Section:**	NN
Approved Inspection and Test Plan:	L01-MBLC-CON-ARC-ITP-006068-R00	**Clause:**	NN
Clearance Form Enclosed:	☐ Yes / Disciplines (.....)		☒ No

Approved Drawing No.:	L01-MBLC-D05-IWW-DWG-10BD100-01-LAY9096 L01-MBLC-D05-IWW-DWG-10BD100-01-LAY9095	Attached Approved Drawings	☒
Location / Level / Room Name & No. / Grid Line:	Zone 17 (First Floor)	Attached Location Sketch	☒
		Attached Check Sheet	☒
		Attached Previous Revision (if any)	☐

The above work has been completed according to Project requirements and specifications and is ready for inspection

MBL Construction Representative:

Name:	**Issam Alkhatib**	**Signature:**		**Date:**	09/03/24

MBL QA/QC's Manager:

Name:	**Yazan Shoqeir**	**Signature:**		**Date:**	09/03/24

Supervision Consultant's Review:

Checks:
Site Test Results (if any): ☐ Passed ☐ Failed ☐ Not Applicable

Status of Inspection: ☑ Status A (Approved) ☐ Status B (Approved with Comments) ☐ Status C (Objection)

Comments:
Suspension system of wooden droped beams is accepted.
10/3/24
11/03/24 M. Atahwi.

Reviewer Name:		**Signature:**		**Date:**	11/3/2024

PMCM's Review:

Endorsement: ☑ Yes ☐ No

Comments:

☐ To be Re-submit

Reviewer Name:	T. Ignacio	**Signature:**		**Date:**	13/3/24

Note: This site inspection does not relieve the contractor from any of his contractual obligations.

PARSONS dar MBL MODERN BUILDING LEADERS (MBL) Co. LLC

Received

Work Inspection Request

Request Ref.:	L01-MBLC-CON-ARC-WIR-010493	Revision:	R00	Submission Date:	15/02/24
Project:	L01-01	Inspection Date:	17/02/24	Time:	11:00
Client:	CPPA	Project/Zone No:	L01/17		
PMCM/Engineer:	Saudi Arabian Parsons Ltd	Contractor:	MBL		

Discipline:

☐ Survey ☐ Civil ☒ Architectural ☐ Structural ☐ Landscape
☐ Electrical ☐ Low current ☐ Mechanical ☐ HSE ☐ Testing/Commissioning
☐ Facade ☐ Others (.....) Sub- discipline (Steel Structure)

Work Details:

Description:
INSPECTION FOR (CEILING SUSPENTION SYSTEM) IN FIRST FLOOR ZONE 17- CORRIDOR 5: (FF-Z2-73)

Approved Method Statement:	L01-MBLC-CON-ARC-MES-006192-R00	Section:	NN
Approved Inspection and Test Plan:	L01-MBLC-CON-ARC-ITP-006068-R00	Clause:	NN
Clearance Form Enclosed:	☐ Yes / Disciplines (.....)		☒ No

Approved Drawing No.:	L01-MBLC-D05-IWW-DWG-10BD100-01-LAY9096 L01-MBLC-D05-IWW-DWG-10BD100-01-LAY9095	Attached Approved Drawings	☒
		Attached Location Sketch	☒
		Attached Check Sheet	☒
Location / Level / Room Name & No. / Grid Line:	Zone 17 (First Floor)	Attached Previous Revision (if any)	☐

The above work has been completed according to Project requirements and specifications and is ready for inspection

MBL Construction Representative:

Name:	Issam Alkhatib	Signature:		Date:	15/02/24

MBL QA/QC's Manager:

Name:	Yazan Shoqeir	Signature:		Date:	15/02/24

Supervision Consultant's Review:

Checks:
Site Test Results (if any): ☐ Passed ☐ Failed ☐ Not Applicable

Status of Inspection: ☐ Status A (Approved) ☐ Status B (Approved with Comments) ☒ Status C (Objection)

Comments:
* Area of inspection shall be specified on attached drawings.
* Clearance should be attached.

Reviewer Name:		Signature:		Date:	18/2/2024

PMCM's Review:

Endorsement: ☐ Yes ☐ No

Comments:
RESUBMIT

☒ To be Re-submit

Reviewer Name:		Signature:		Date:	19/2/2024

Note: This site inspection does not relieve the contractor from any of his contractual obligations

Client	PMC PARSONS	CSC dar	Contractor: MBL
Project Name: L01, Riyadh, Saudi Arabia	Description: Inspection and Test Plan for WOOD WORKS		Document Ref No. L6493

5.2 Appendix 2

Check List for Wood Works

Date							
Location:							
Stage	Item	MBLC		DAR	Date	Remarks
		Satisfied	Unsatisfied	Check		
Approval	Material Approval					
	Sample /Mockup					
	Method statement approval					
	ITP & Risk assessment approval					
	Drawings and Details					
Leveling and location check	Location and levels as per approved shop drawings					
Clearance	MEP & Structure Clearance					
Suspension System installation	Tie road installation					
	The parameter angle installation					
	Accessories					
Application of Installation of Wood panels	Wood type, thickness, and dimensions	✓				
	Check panels Installation As per approved drawings	✓				
Finishing & Retouches						

MBLC Site Engineer		MBL QC Engineer		Consultant Engineer	
Name:		Name:		Name:	M.AtAhmed
Signature		Signature		Signature	
Date		Date		Date	18/3/24

Previous # 10492

TRANSMITTAL FORM

Transmittal Ref.	L01-DARH-MBLC-CON-TRN-004023	**Date**	05-Oct-2023
Program	Construction Supervision Services (CSC)		

Project	L01	**Scope**	L01-01 Office Complex

From CSC	Dar AL Handasah (Shair and Partners)
To CSC	**Modern Building Leaders Co. - MBLC**
Attention to	**Khalil Atieh**
Copy to	SAPL and F+G Document Management Department

Enclosures

☐ Drawings ☐ Letters ☐ Reports ☐ Subcon Prequalification ■ Material Submittal
☐ Schedule / Plan ☐ Samples ☐ Specifications ☐ Other

Submitted

☐ For Approval ☐ As Requested ☐ For Review & Comments ■ Other For Information & Action

Item Details

SN	Description	Media	Reference No.	Rev	Status
1	L01-01-01 - Wood Joinery Works	Email	L01-MBLC-CON-ARC-MAT-006127	01	*B*

********** Nothing Follows**********

Remarks:

Please find the attached 'DAR comments (CSC)' for the mentioned above.

In response to MBL TRN Ref # L01-MBLC-DARH-CON-TRN-023995

Transmitted by

Name	Louai Krishan	**Signature**		**Date**	05-Oct-2023

Received by

Name		**Signature**		**Date**	

dar

DAR Comments Sheet (DCS)

Project Name	L01 - Yamama Building Offices	Project No.	S20066-0100S
Client	Crown Prince Private Affairs (CPPA)	Project Management Consultant (PMC)	PARSONS
Construction Supervision Consultant (CSC)	DAR Al Handasah (DAR)	Main Contractor	Modern Building Leaders (MBL)

Transmittal Ref. No.	L01-MBLC-DARH-CON-TRN-023660			Transmittal Date			29-Sep-23
Document Ref. No.	L01-MBLC-CON-ARC-MAT-006148	Revision	00	Document Type	MAT	Discipline	Architectural
Document Description/Subject	L01-00-00 Wood Ceiling Suspension System						

DAR Comments / Replies Legends & Status	Comment Code Legend (for individual comments): 1= Action Required; 2 = Note/Recommendations	Reply Code Legend: I = Incorporated; II = Not incorporated for reason stated in reply	Open / Closed

No.	Initial	Page / Section / Doc	Comment Code	Reviewer Comment	Reply Code	Main Contractor Reply	Reply Status by Reviewer
1	ME	General	1	The contractor shall highlight/identify the selected items (threaded rods, angle supports, nuts, and screws), in accordance with the approved structural calculations interms of dimensions, thickness, grade…etc.			
2	ME	General	1	A physical Samples for each suspension system membershall be provided to obtain all required approvals prior to material delivery.			
3	ME	General	1	It is required to perform the required field tests, specifically a pull-out test, for the implemented ceiling suspension system.			
4	ME	General	1	It is necessary to securely fasten double nuts at the bottom of the threaded rod.			
5	ME	General	1	The contractor shall comly with all PMC comments on the calculation note.			

"The submittal is coded "Approved as noted" – Code 'B', subject to the approval of related final design deliverables (Drawings, Specifications and Technical Reports) and shop drawings. The Contractor shall take all liability for proceeding and purchasing materials based on this approval with comments, absolving CPPA, SAPL and DAR from any subsequent liability and action. Also, the Contractor shall be fully responsible to ensure that design and procured material are fit for purpose including but not limited to full suitability of the procured material to the design requirements in terms of capacities, types and specifications while at the same time ensuring that the design properly consider any approved material in terms of space allocation and any applicable considerations. Noting that such approvals and consents shall in no way provide any relief, whether in whole or in part, to the Design and Build Contractor from any of its obligations and duties."

Review Status Code:	B	A - Approved	B - Approved as Noted	C - Revise & Resubmit	D - Rejection

Construction Supervision Consultant (CSC)				Main Contractor	
Reviewer Name(s)	Initials	Position	Signature	Date	Document Type Legend:
Mohammed Odibat	ME	Architectural Engineer		4/10/2023	MAT: Material Submittal MES: Method Statement
Louai Krishan	LK	Resident Engineer		4/10/2023	ITP: Inspection & Test Plan

"Approval shall not relieve Contractor of his liabilities under the Contract or constitute authorization of any change in Contract Documents".

8

Consultant: PARSONS	Client:	Contractor: MBL MODERN BUILDING LEADERS (MBL) Co. LLC شركة قادة البناء الحديث المحدودة
Project Name: L01, Riyadh, Kingdom of Saudi Arabia	Description:	Document Reference No: 9148

CLEARANCE FOR CEILING

Ref No: L01-BT-ARC-CLR-00099

Date: 28/10/2023 07/01/24

Location / Level / Room Name & No. / Grid Line	Room No: FF-Z2-73/Zone-17/ at First Floor					
				REMARK		
DISCIPLINE	SUB-CONTRACTOR	MBL QA/QC	CONSULTANT	SUB-CONTRACTOR	MBL	DAR
MECHANICAL			9.1.24	As per Attach list	As Per Attach Mech Sheet	No objection only future change contractor Responsibility
ELECTRICAL		Rami 1/11/2023	07/01/24	As per Attach list	As Per Attached Sheet	No objection Any future change is contractors sole responsible
LOW CURRENT/BMS	04/11/23		9.1.24	As per Attached List		ELV. No objection
CIVIL						
SURVEY						
STEEL STRUCTURE						
FACADE						

Comments :

Civil Site Engineer	Civil QA/QC Engineer	Consultant Engineer
Name:	Name:	Name: M. Al-Ahmad
Signature:	Signature:	Signature:
Date:	Date:	Date: 10/1/24.

* curtain control system not finalized.

SAPL
SAUDI ARABIAN PARSONS LTD
شركة بارسونز العربية السعودية المحدودة

dar

MBL
MODERN BUILDING LEADERS (MBL) Co. LLC
شركة قادة البناء الحديث المحدودة

L01 PROJECT - RIYADH, KSA
MATERIAL SAMPLE (MATCHING)

Discipline:	**Architectural**
Submittal Ref:	**L01-MBLC-CON-ARC-SMP-000507-R00**
MAT Ref.:	
Description:	**WD03 – African Mahogany (Matching sample)**
Area of application	**L01 – Minister's office 8**
Approved By Vesta/MBL	
Name:	AHMED MALAGUN
Signature:	
Date:	11/12/23
Approved By MBL Quality	
Name:	**Khaled Naim Sabha**
Signature:	
Date:	
Approved By Parson	
Name:	
Signature:	
Date:	
Approved By CPPA	
Name:	
Signature:	
Date:	

Comment:

SAPL
SAUDI ARABIAN PARSONS LTD
شركة بارسونز العربية السعودية المحدودة

dar

MBL
MODERN BUILDING LEADERS (MBL) Co. LLC
شركة قادة البناء الحديث المحدودة

L01 PROJECT -RIYADH, KSA
MATERIAL SAMPLE

Discipline:	**Architectural**
Submittal Ref:	**L01-MBLC-CON-ARC-SMP-000114-R00**
MAT Ref.:	
Description:	~~Brazilian Mahogany~~ [redacted] African B
Name:	**Khaled Naim Sabha**
Area of application	**Main Building - HRH OFFICE T&W**
Signature:	
Date:	**23-August-2022**
Approved By Vesta	
Name:	ALBERTO CHIARIBELLI
Signature:	
Date:	25/8/22
Approved By Parson	
Name:	THOMAS BLICHER
Signature:	
Date:	25/8-22
Approved By CPPA	
Name:	
Signature:	
Date:	

GF-Z3-XX
MINISTER'S OFFICE 8

12/10/22

VESTA

EST. 1956

B DESIGN

THE STORE

FRONT

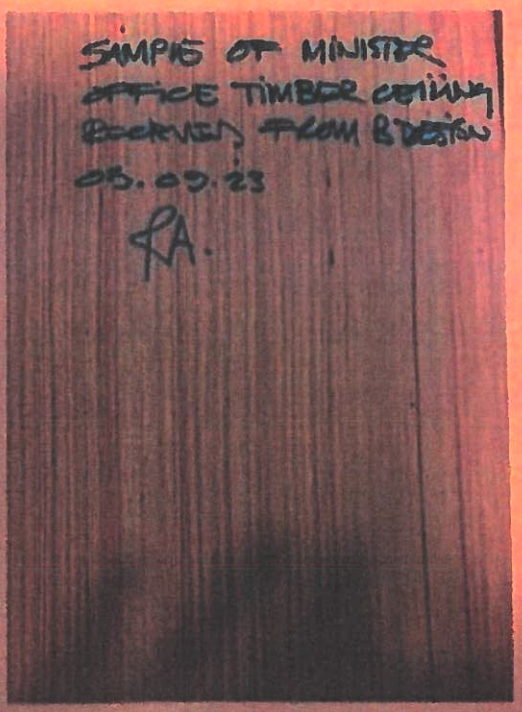

BACK

PHYSICAL APPROVED SAMPLE

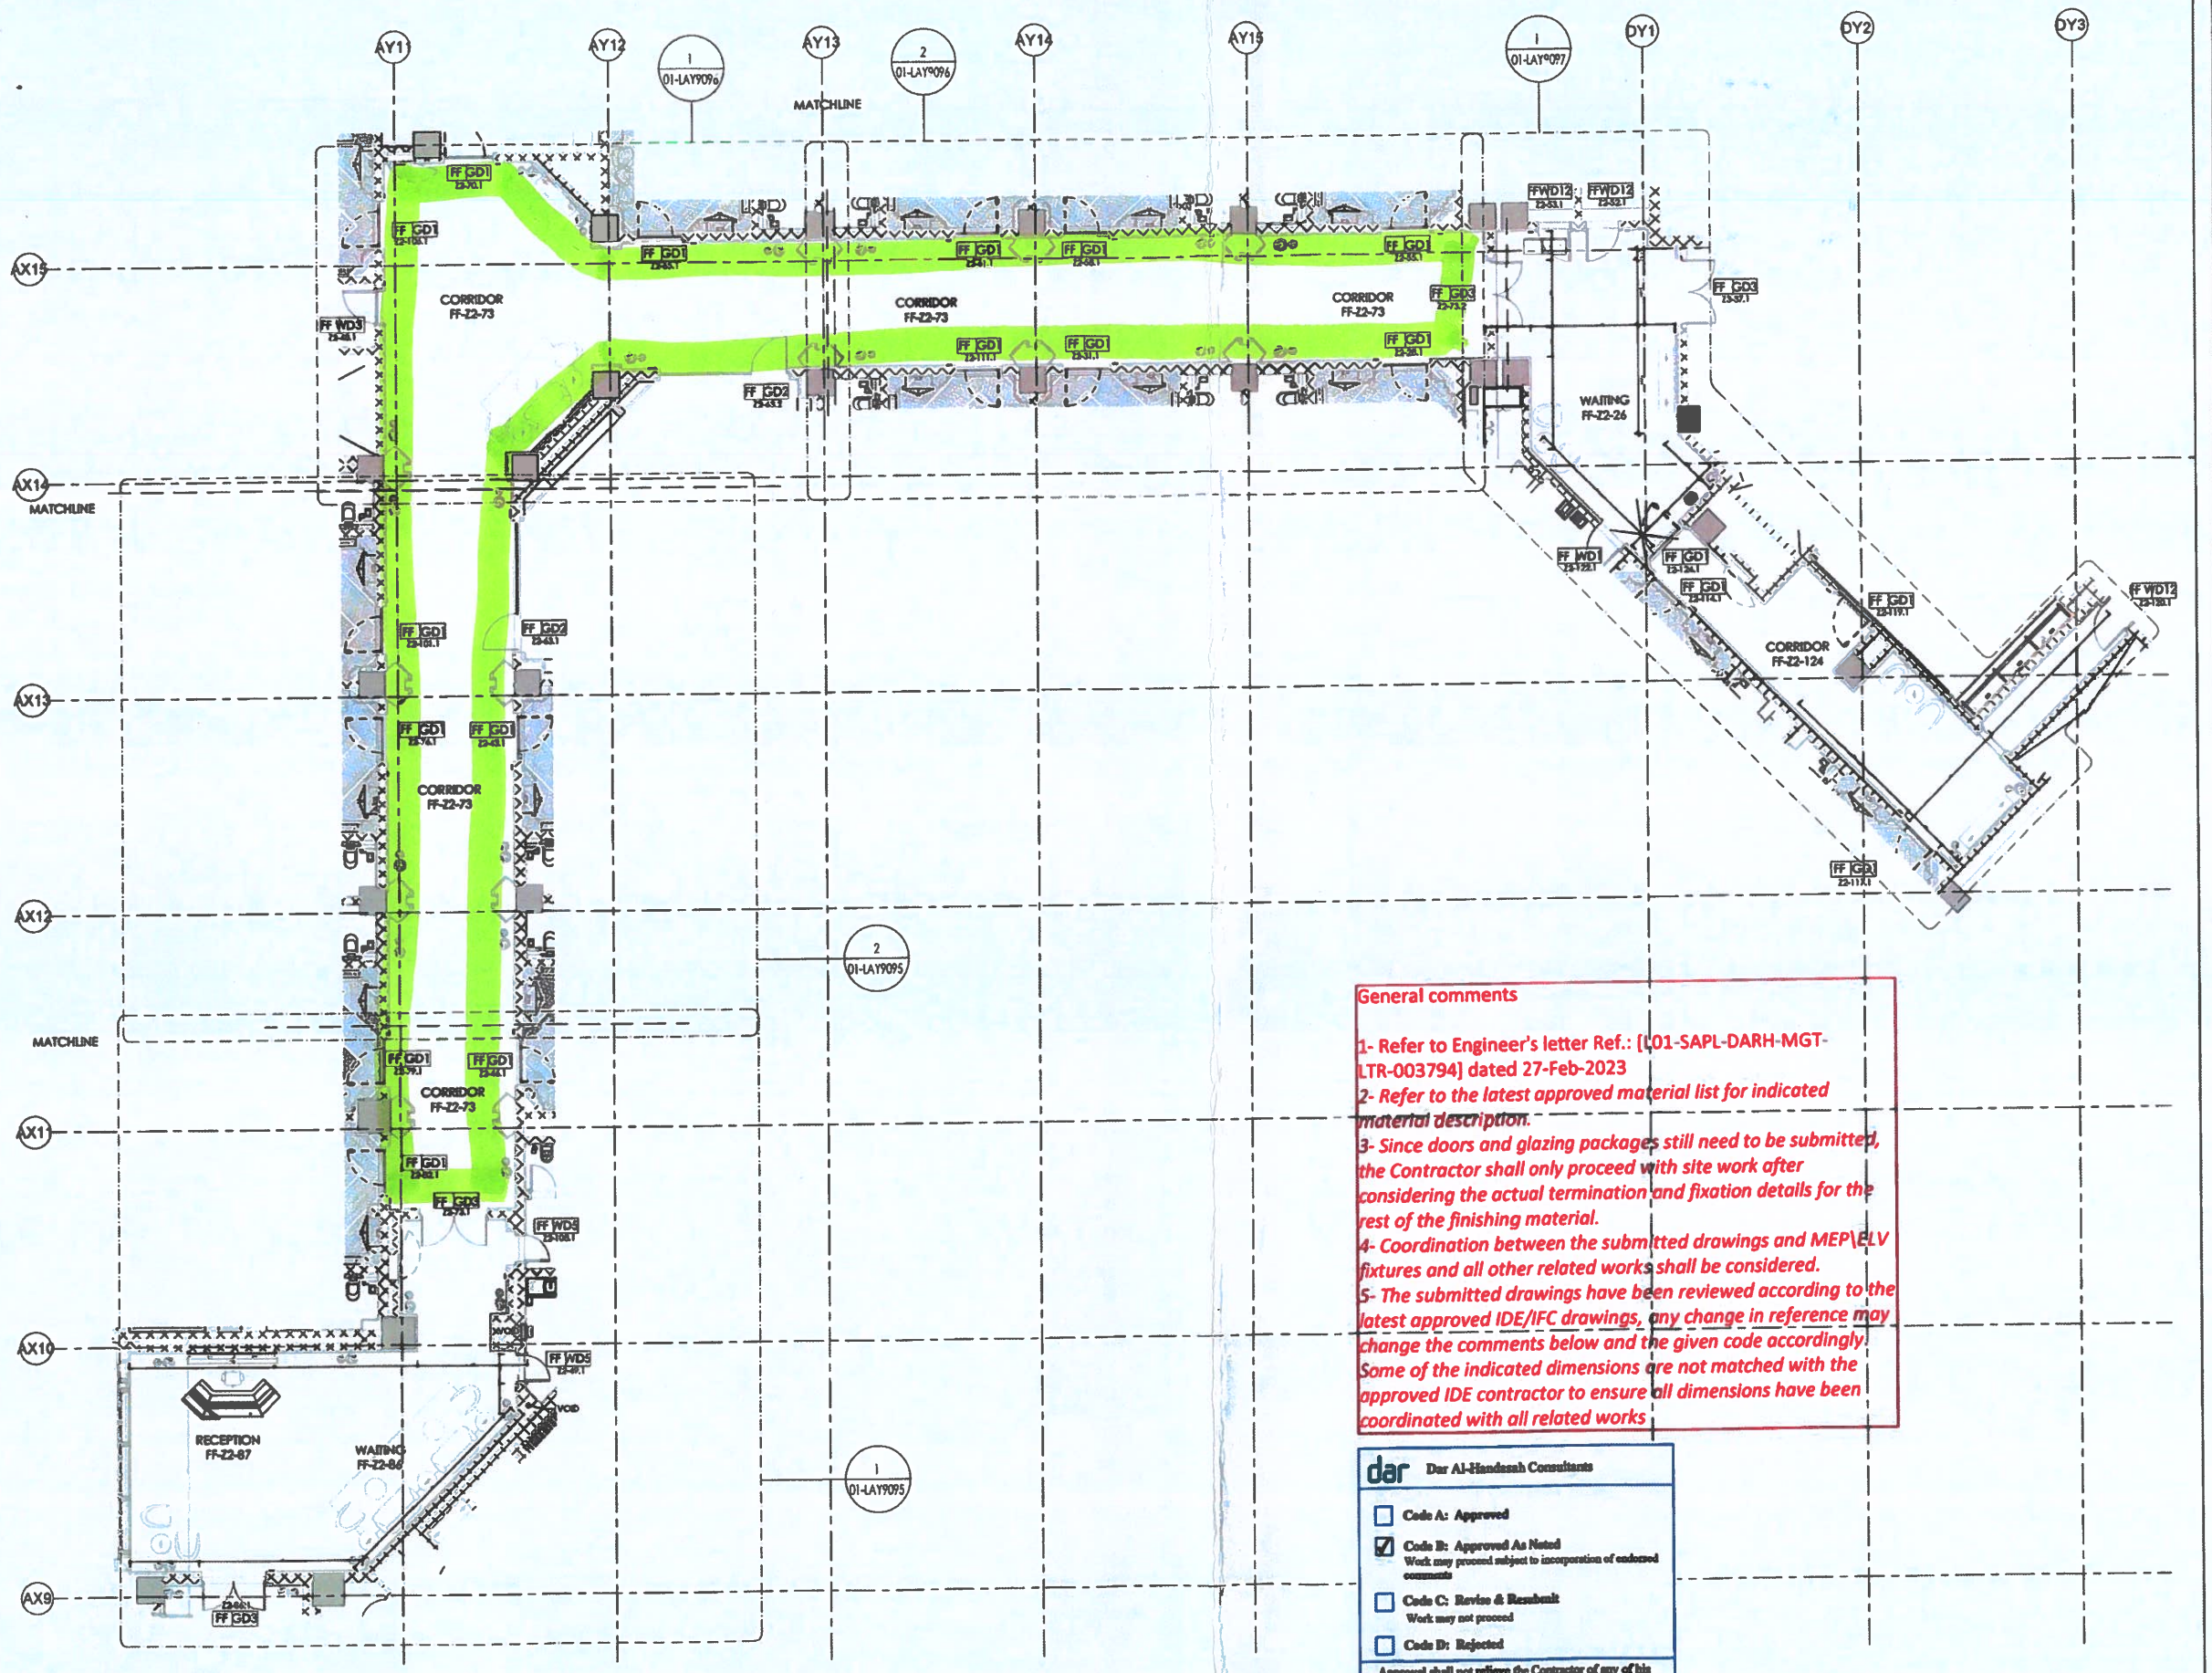

1 OVERALL ARCHITECTURAL INFORMATION PLAN
01-LAY9095 SCALE 1 : 75 @ A0

General comments

1- Refer to Engineer's letter Ref.: [L01-SAPL-DARH-MGT-LTR-003794] dated 27-Feb-2023
2- Refer to the latest approved material list for indicated material description.
3- Since doors and glazing packages still need to be submitted, the Contractor shall only proceed with site work after considering the actual termination and fixation details for the rest of the finishing material.
4- Coordination between the submitted drawings and MEP\ELV fixtures and all other related works shall be considered.
5- The submitted drawings have been reviewed according to the latest approved IDE/IFC drawings, any change in reference may change the comments below and the given code accordingly. Some of the indicated dimensions are not matched with the approved IDE contractor to ensure all dimensions have been coordinated with all related works

dar Dar Al-Handasah Consultants

- [ ] Code A: Approved
- [x] Code B: Approved As Noted — Work may proceed subject to incorporation of endorsed comments
- [ ] Code C: Revise & Resubmit — Work may not proceed
- [ ] Code D: Rejected

Approval shall not relieve the Contractor of any of his obligations under the Contract or constitute authorization of any change to Contract Documents or variation to the works. Contractor is responsible for dimensions, quantities and coordination with other trades.

Name: Mohammad Eqbal Date: 23/05/23

GENERAL NOTES

PART KEY PLAN

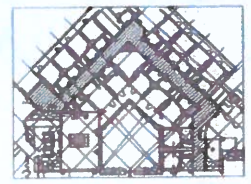

REVISIONS			
REV	DATE	DESCRIPTION	APPROVED
00	19/04/2023	ISSUED FOR APPROVAL	

OVERALL KEY PLAN

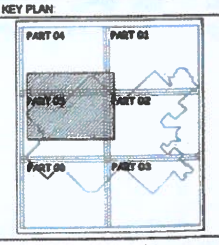

PROJECT MANAGEMENT CONSULTANT: PARSONS

MAIN CONTRACTOR: MBL

SUB CONTRACTOR: Saudi Build Design Co.

PROJECT TITLE: L01- SCOPE 2
Riyadh - Saudi Arabia

DRAWING TITLE: CORRIDOR 5 OVERALL ARCHITECTURAL INFORMATION PLAN

JOB NO.	ACTUAL SIZE	DRAWN	CHECKED
L01	A0	H.U/MTQ	S.B
	SCALE	DESIGNED	APPROVED
DWG NO.	AS INDICATED	-	-

L01-MBLC-D05-IWW-DWG-10BD100-01-LAY9095

STATUS	DATE	REVISION
SHOP DRAWING	19/04/2023	00

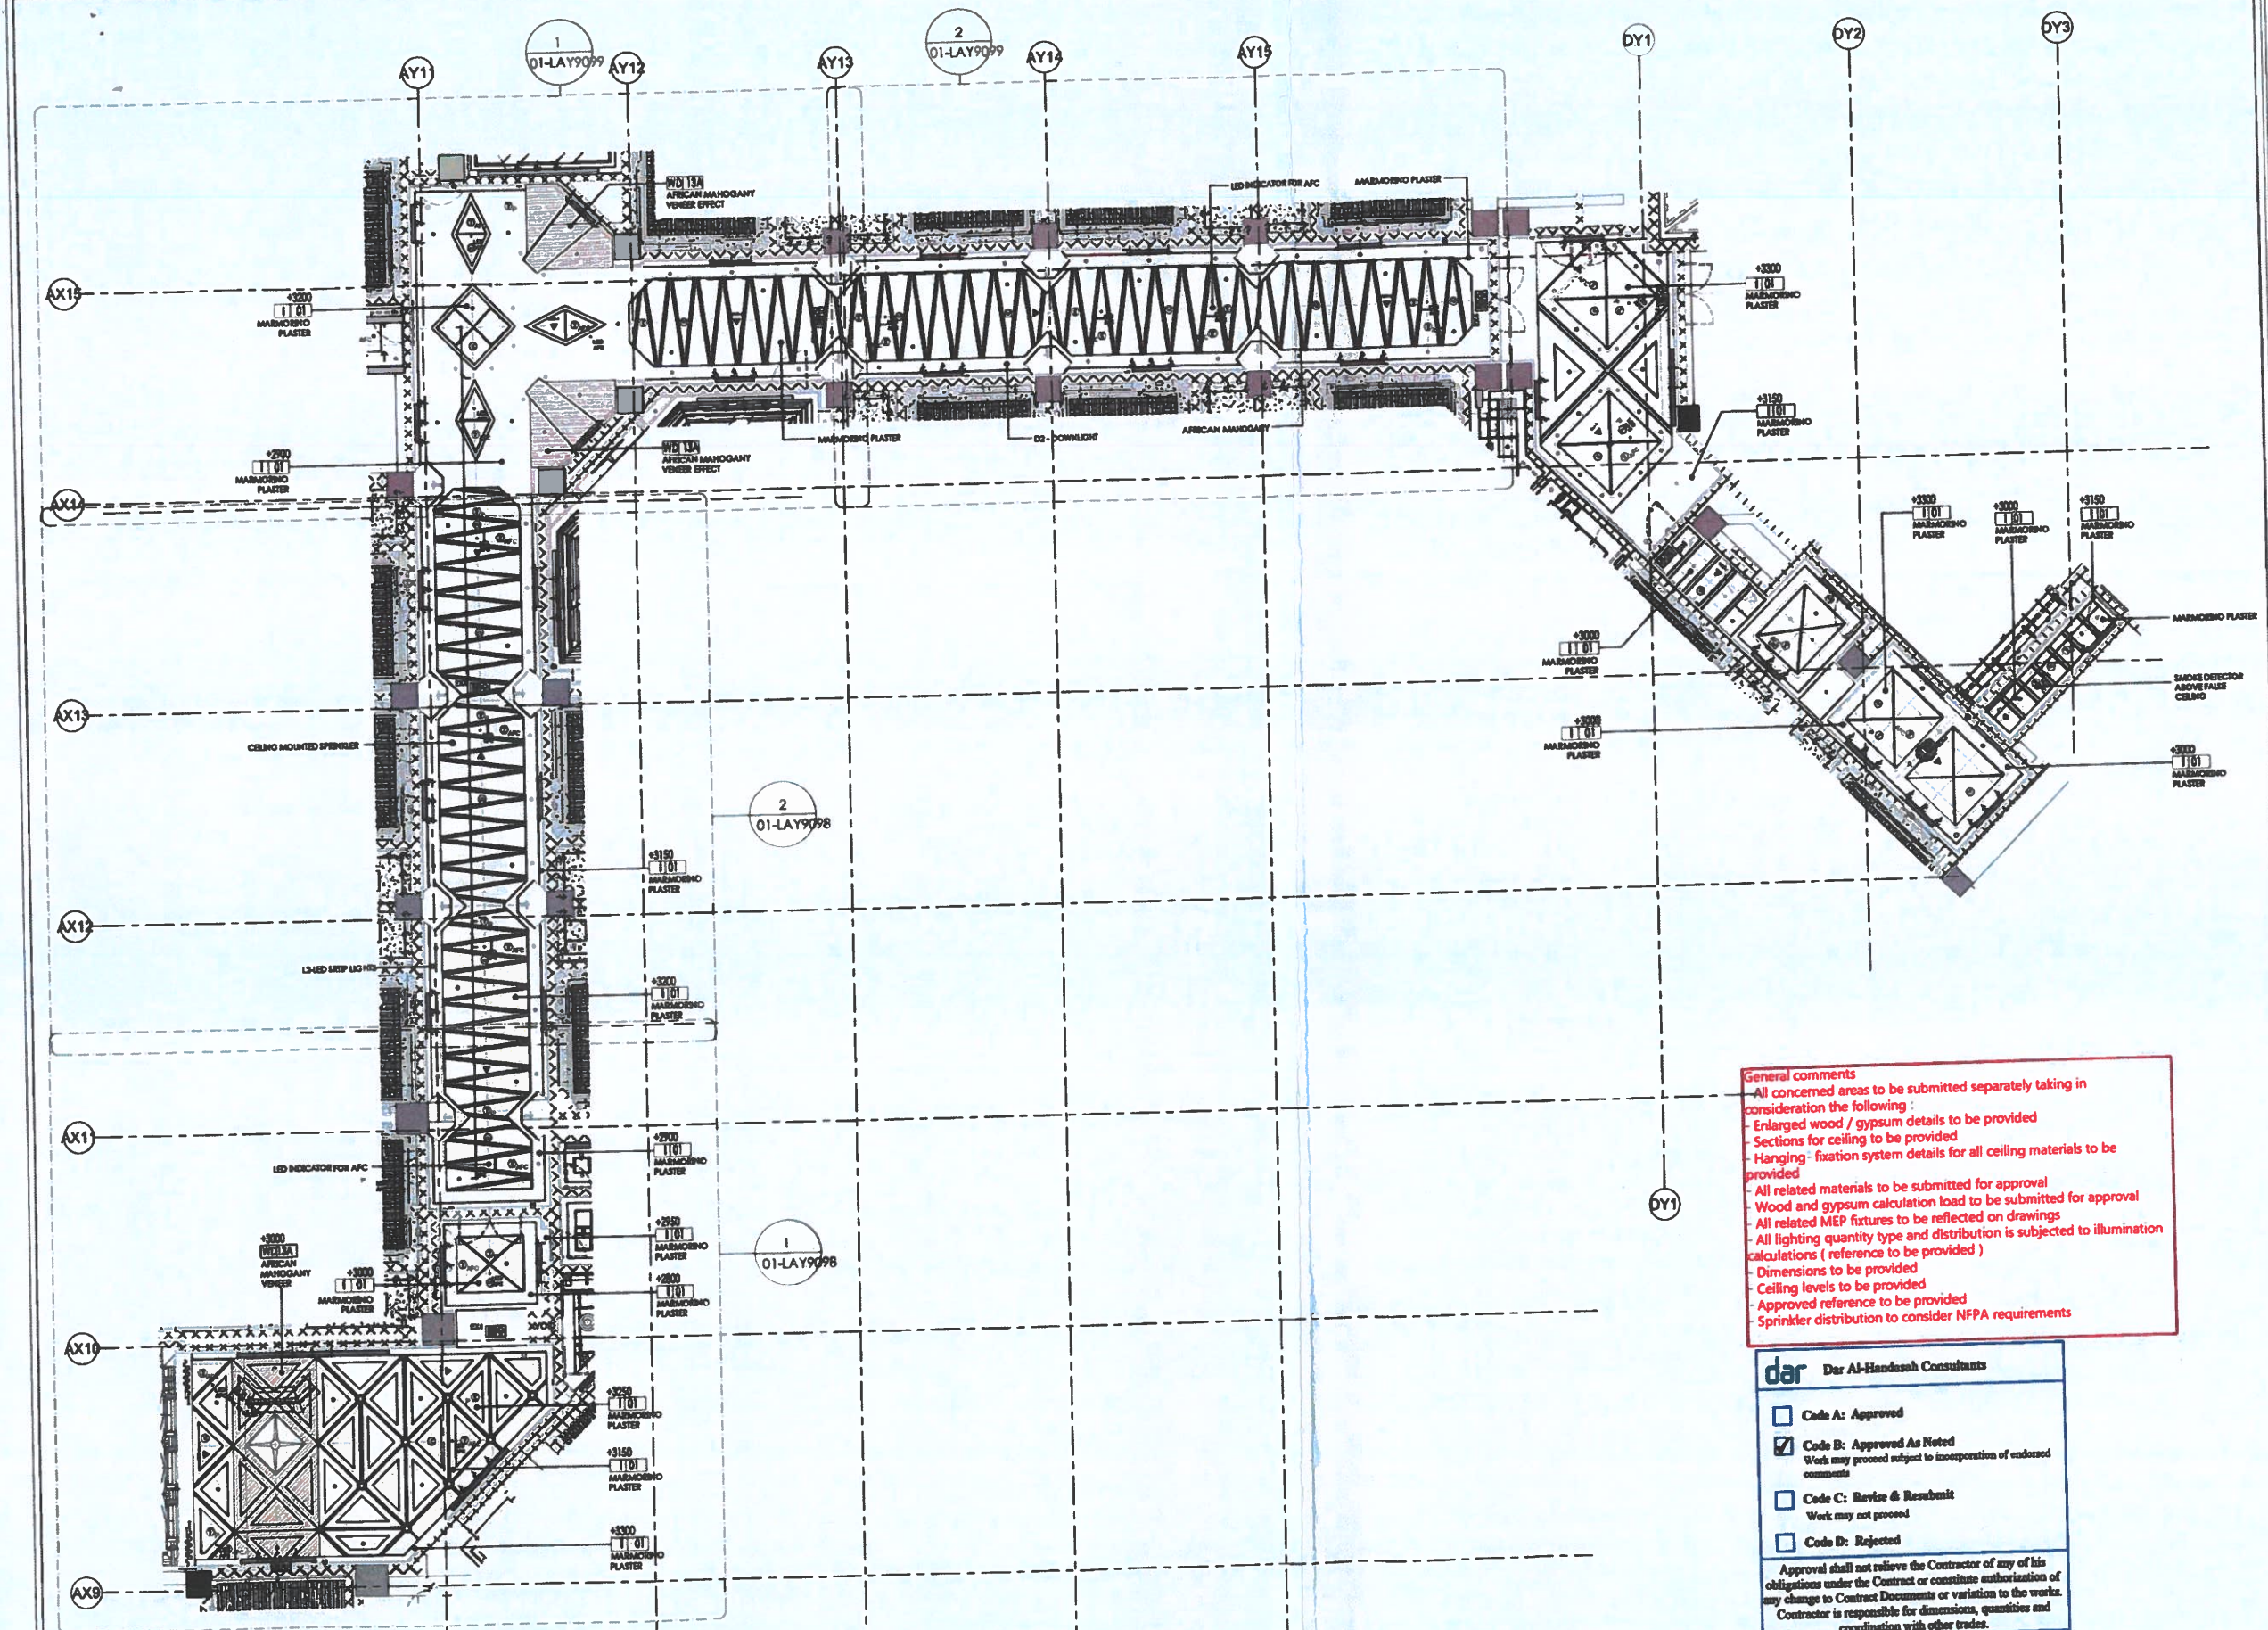

1 OVERALL REFLECTED CEILING PLAN
01-LAY9098 SCALE 1 : 75 @ A0

GENERAL NOTES

General comments
All concerned areas to be submitted separately taking in consideration the following :
- Enlarged wood / gypsum details to be provided
- Sections for ceiling to be provided
- Hanging- fixation system details for all ceiling materials to be provided
- All related materials to be submitted for approval
- Wood and gypsum calculation load to be submitted for approval
- All related MEP fixtures to be reflected on drawings
- All lighting quantity type and distribution is subjected to illumination calculations (reference to be provided)
- Dimensions to be provided
- Ceiling levels to be provided
- Approved reference to be provided
- Sprinkler distribution to consider NFPA requirements

dar Dar Al-Handasah Consultants

- [ ] Code A: Approved
- [x] Code B: Approved As Noted
  Work may proceed subject to incorporation of endorsed comments
- [ ] Code C: Revise & Resubmit
  Work may not proceed
- [ ] Code D: Rejected

Approval shall not relieve the Contractor of any of his obligations under the Contract or constitute authorization of any change to Contract Documents or variation to the works. Contractor is responsible for dimensions, quantities and coordination with other trades.

Name: Mohammad Eqbal Date: 23/05/23

PART KEY PLAN

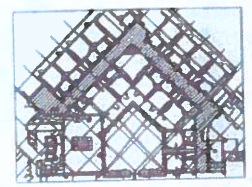

REVISIONS:

REV	DATE	DESCRIPTION	APPROVED
00	19/04/2023	ISSUED FOR APPROVAL	

OVERALL KEY PLAN:

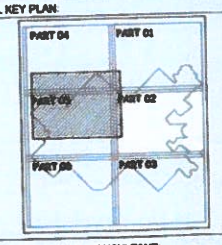

PROJECT MANAGEMENT CONSULTANT:
PARSONS

MAIN CONTRACTOR:
MBL

SUB CONTRACTOR:

PROJECT TITLE:
L01- SCOPE 2
Riyadh - Saudi Arabia

DRAWING TITLE:
CORRIDOR 5
OVERALL REFLECTED CEILING PLAN

JOB NO.	ACTUAL SIZE	DRAWN	CHECKED
L01	A0	H.UMITQ	S.S
	SCALE	DESIGNED	APPROVED
DWG NO.	AS INDICATED	-	-

L01-MBLC-D05-IWW-DWG-10BD100-01-LAY9098

STATUS	DATE	REVISION
SHOP DRAWING	19/04/2023	00